

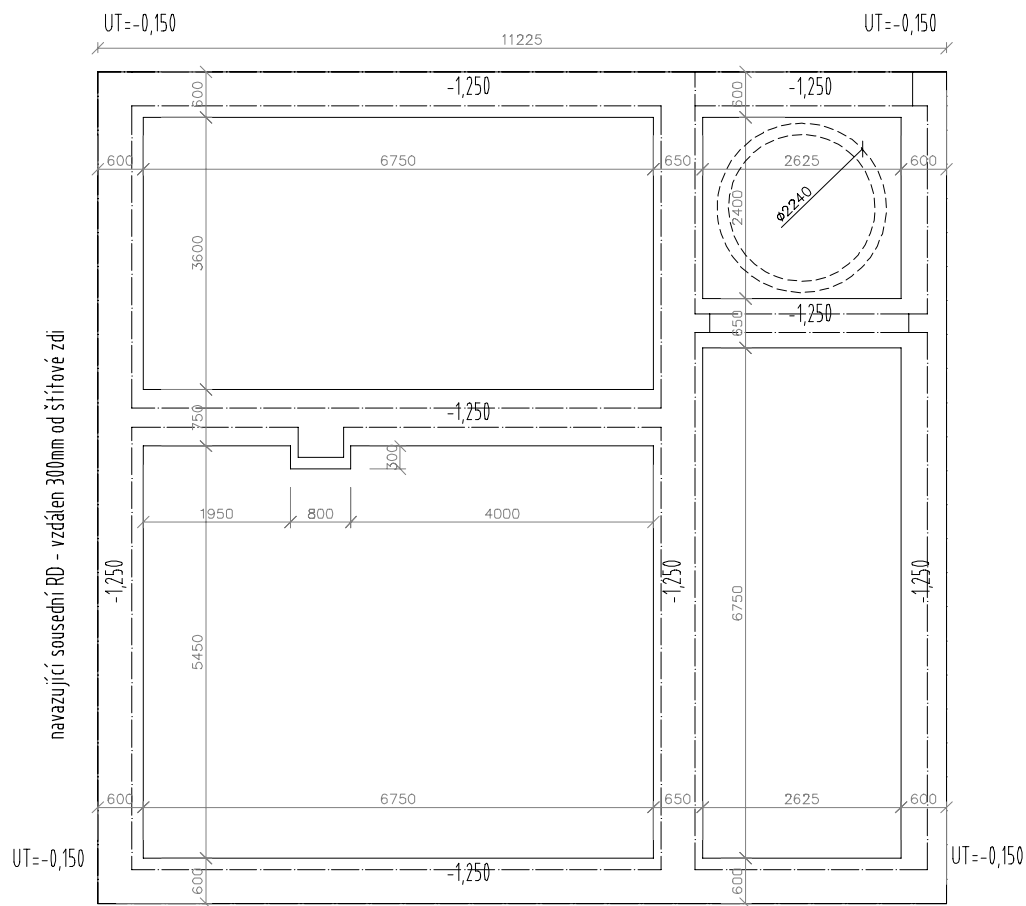


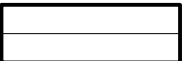

LEGENDA MATERIÁLŮ:

-  Základové konstrukce budou z prostého betonu C 25 / 30 XC1
-  Jímka na splašky AS 6,7 PB/EO k zabetonování

Poznámka: Základovou spáru převezme před betonáží statik!!! V případě jílovitého podloží bude základová spára min 1,4m pod U.T. Do základů bude umístěn zemnící pásek. Na hranici se sousedním objektem bude základová spára v úrovni základů sousedního objektu.

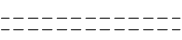

AUTORIZOVANÁ OSOBA		VYPRACOVALI		
ING. ARCH. JIŘÍ BRADÁČ (ČKA 1343)		ING. ARCH. JAN KOKEŠ, ING. ARCH. VÁCLAV KOKEŠ, ING. ARCH. ZDENĚK POSPÍŠIL		
STAVEBNÍK: Ing. Vladimír Grmela, MUDr. Lucie Grmelová, Stará Cihelna 807, 68442 Modřice				
KRAJ: JIHO-MORAVSKÝ				
NÁZEV AKCE: NOVOSTAVBA RD p.č. 1292/40 a 1295/2, k.ú. Modřice			ÚČEL: ÚZEMNÍ SOUHLAS A OHLÁŠENÍ STAVBY	
			DATUM: 07 / 2023	
NÁZEV VÝKRESU: ZÁKLADY			MĚŘÍTKO 1:100	ČÍSLO VÝKRESU: 1