


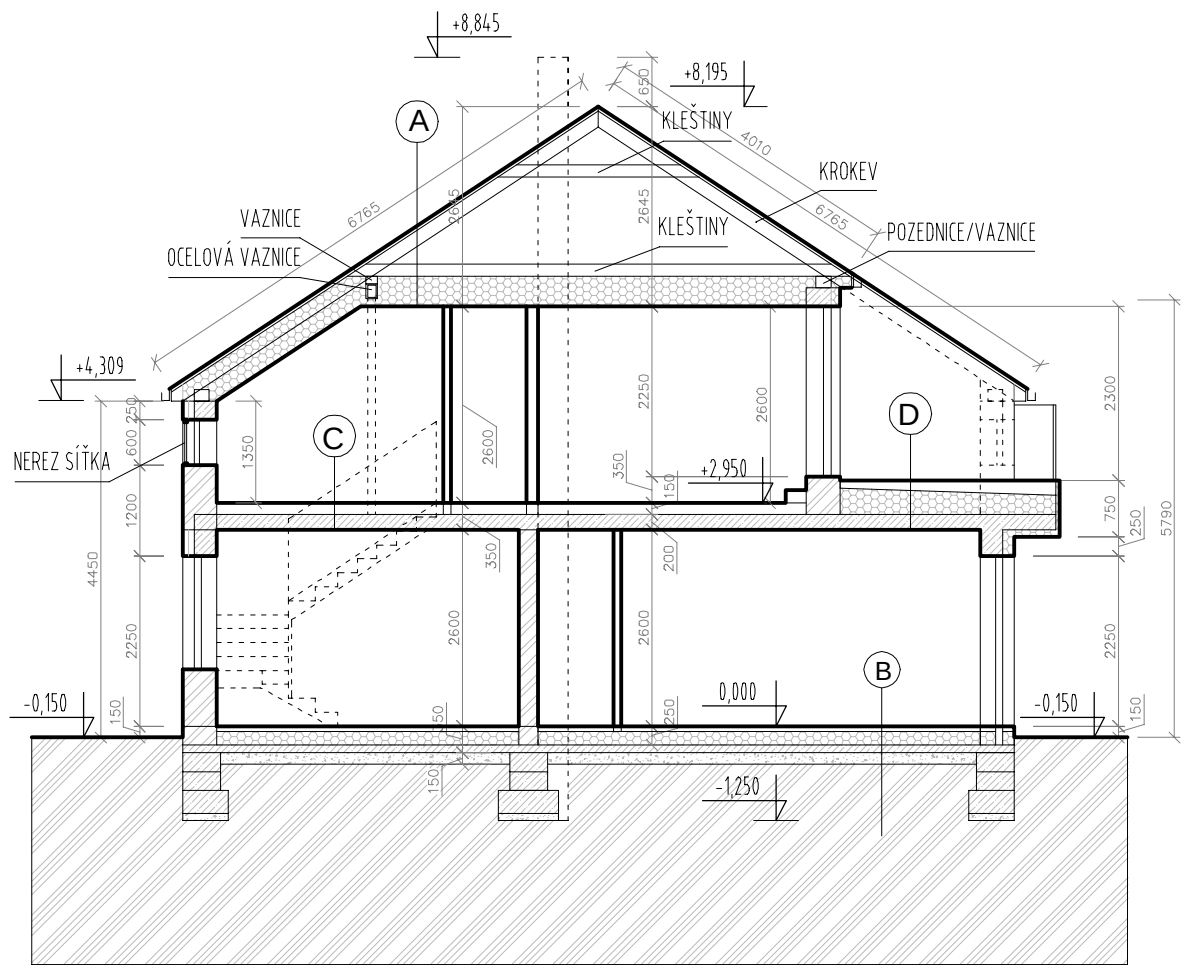

LEGENDA MATERIÁLŮ

- cihelný blok 450 mm a 250 mm
- TI - min. vlna, polystyren EPS, XPS
- příčky z SDK nebo porobetonu - tl. 100, 150 mm
- železobeton
- šterkodrti

SKLADBY

STŘECHA

- A KERAMICKÁ KRYTINA - BRAMAC TURMALIN
- LATĚ KONTRALATĚ
- POJISTNÁ HYDROIZOLACE
- KROKEV + TI Z MINERÁLNÍ VLNY 350MM
- PAROZÁBRANA
- PODHLÉD - SDK

PODLAHA V 2.NP - PODKROVÍ

- C FINÁLNÍ PODLAHOVÁ VRSTVA - KER. DLAŽBA/DŘEVO 15 mm
- BETONOVÁ MAZANINA 50 mm
- ZVUKOVÁ IZOLACE - EPS - T 30 mm
- ŽELEZOBETONOVÝ MONOLITICKÝ STROP 200 mm
- VÁPENNÁ OMÍTKA ŠTUKOVÁ 10 mm

PODLAHA NA TERÉNU

- B FINÁLNÍ PODLAHOVÁ VRSTVA - KER. DLAŽBA / DŘEVO 10 - 20 mm
- BETONOVÁ MAZANINA 50 mm
- POLYETHYLENOVÁ FÓLIE
- POLYSTYREN EPS-S 180 mm
- HYDROIZOLACE - 2x SBS min. 40 se skelnou rohoží
- PODKLADNÍ BETON VYZTUŽENO KARI SÍTÍ 100 mm
- ŠTĚRKOVÝ PODKLAD 150 mm
- NÁŠYP
- ROSTLÁ ZEMINA

TERASA V 2.NP - PODKROVÍ

- D BET. DLAŽBA NA TERČÍCH 50mm
- MPVC FÓLIE 2 mm
- TEPELNÁ IZOLACE ESP 150S VE SPRÁDU MIN.2% 350 - 250 mm
- PAROZÁBRANA 1xsBS
- ŽELEZOBETONOVÝ MONOLITICKÝ STROP 200 mm
- VÁPENNÁ OMÍTKA ŠTUKOVÁ 10 mm

AUTORIZOVANÁ OSOBA	VYPRACOVALI	
ING. ARCH. JIŘÍ BRADÁČ (ČKA 1343)	ING. ARCH. JAN KOKES, ING. ARCH. VÁCLAV KOKES, ING. ARCH. ZDENĚK POSPÍŠIL	
STAVEBNÍK: Ing. Vladimír Gmela, MUDr. Lucie Gmelová, Stará Cihelna 607, 66442 Modřice		
KRAJ: JIHO-MORAVSKÝ		
NÁZEV AKCE: NOVOSTAVBA RD p.č. 1292/40 a 1295/2, k.ú. Modřice		ÚČEL: ÚZEMNÍ SOUHLAS A OHLÁŠENÍ STAVBY
		DATUM: 07 / 2023
NÁZEV VÝKRESU: ŘEZ	MĚŘÍTKO 1:100	ČÍSLO VÝKRESU: 4